



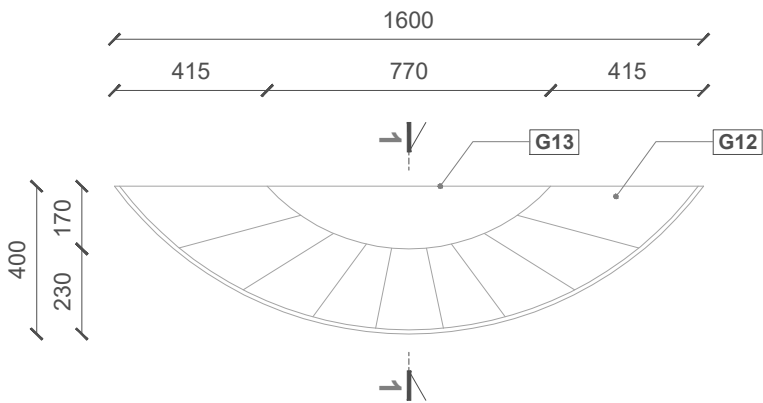


1 MẶT BỀ

TL 1:20 @A3

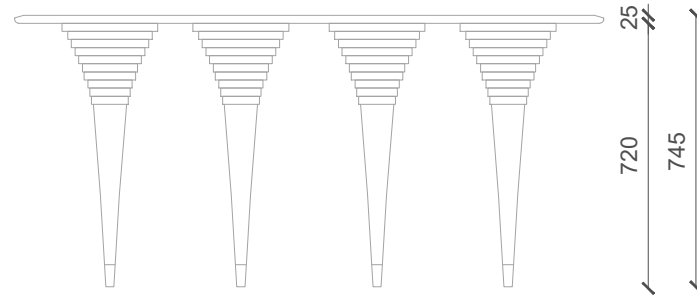


2 MẶT ĐỨNG

TL 1:20

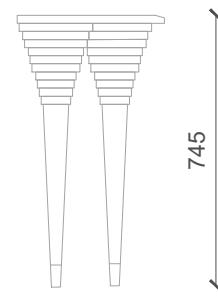


3 MẶT BÊN

TL 1:20

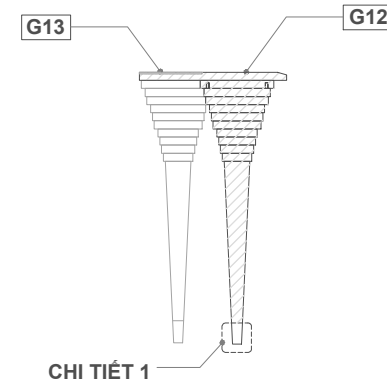


4 MẶT CẮT 1

TL 1:20

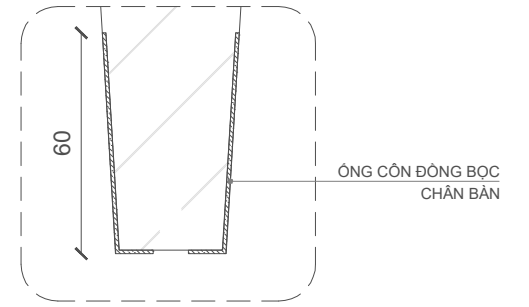


5 CHI TIẾT 1 - CHÂN BÀN

TL 1:2 @A3

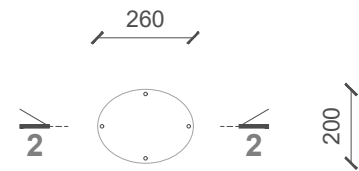


6 CHÂN BÀN - MẶT BỀ

TL 1:20

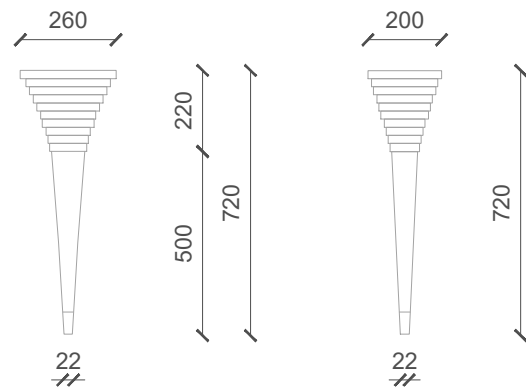


7 CHÂN BÀN - MẶT ĐỨNG & MẶT BÊN

TL 1:20

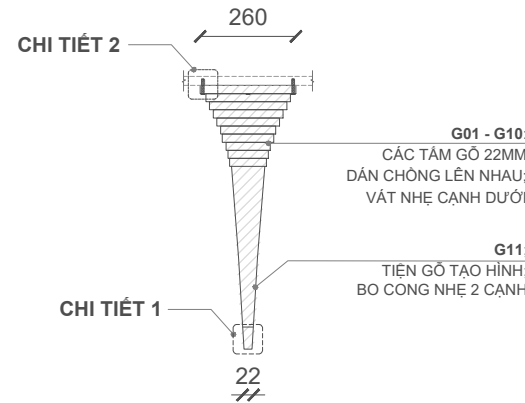


8 CHÂN BÀN - MẶT CẮT 2

TL 1:20

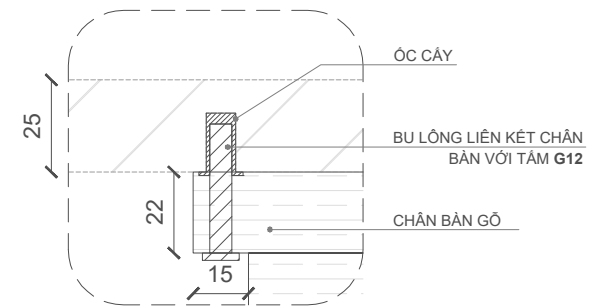


9 CHI TIẾT 2 - LIÊN KẾT CHÂN BÀN VÀ MẶT BÀN

TL 1:4 @A3

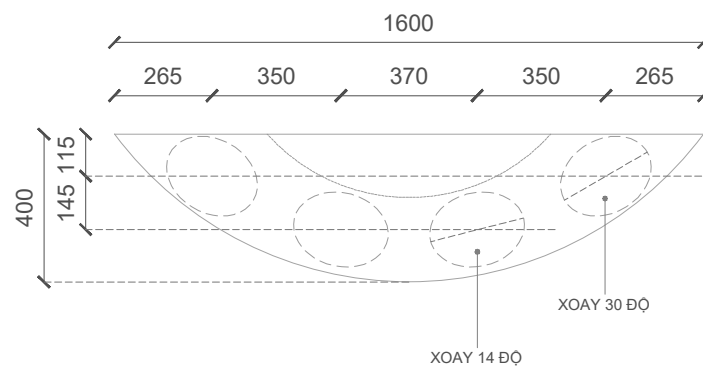

10 CHÚ THÍCH VỊ TRÍ CÁC CHÂN BÀN


TL 1:20

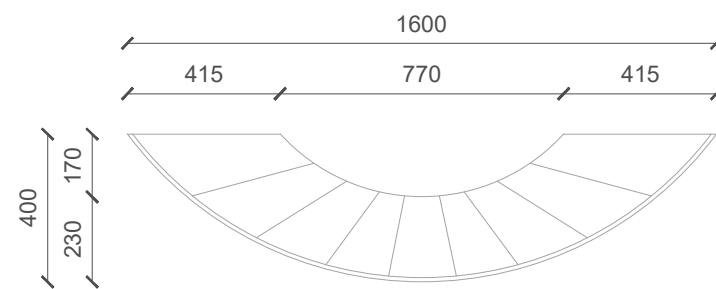

11 KÍCH THƯỚC TẦM G12

TL 1:20

TIỆN GỖ TẠO HÌNH;
VÁT CONG NHẸ 2 BÊN

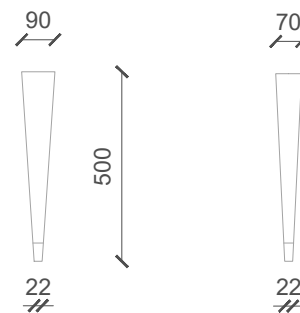


G11 - MẶT ĐỨNG G11 - MẶT BÊN

12 G11 - PHẦN CHÂN TIỆN GỖ

TL 1:20



HÌNH PHỐI CẢNH THAM KHẢO

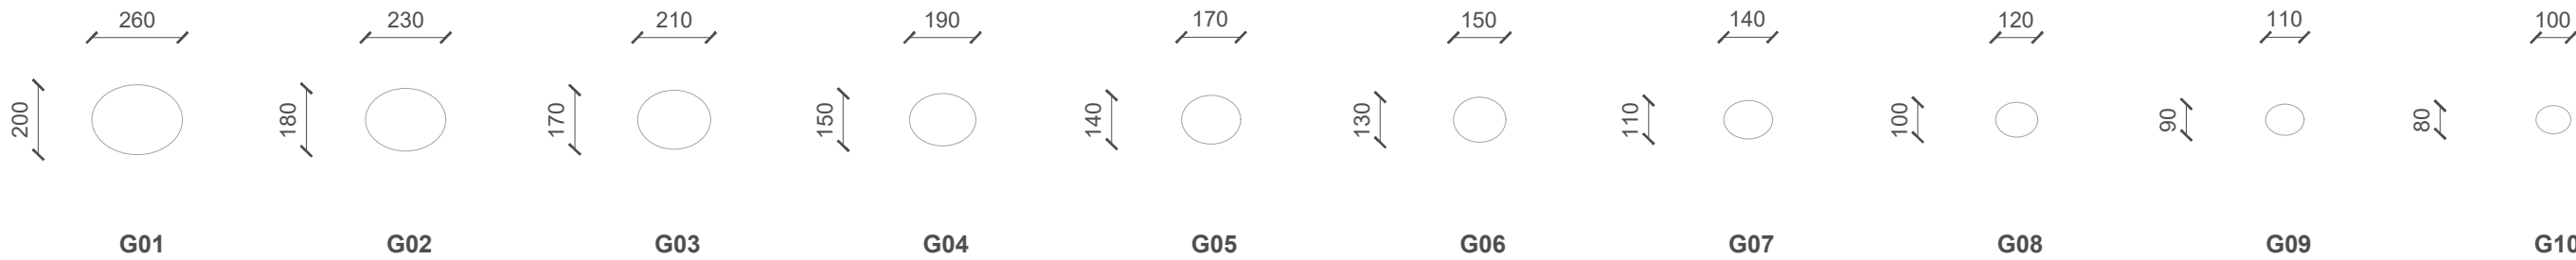

1 CÁCH TẮM GỖ 22MM (G01 ĐẾN G10) - MẶT BẰNG
TL 1:20 @A3